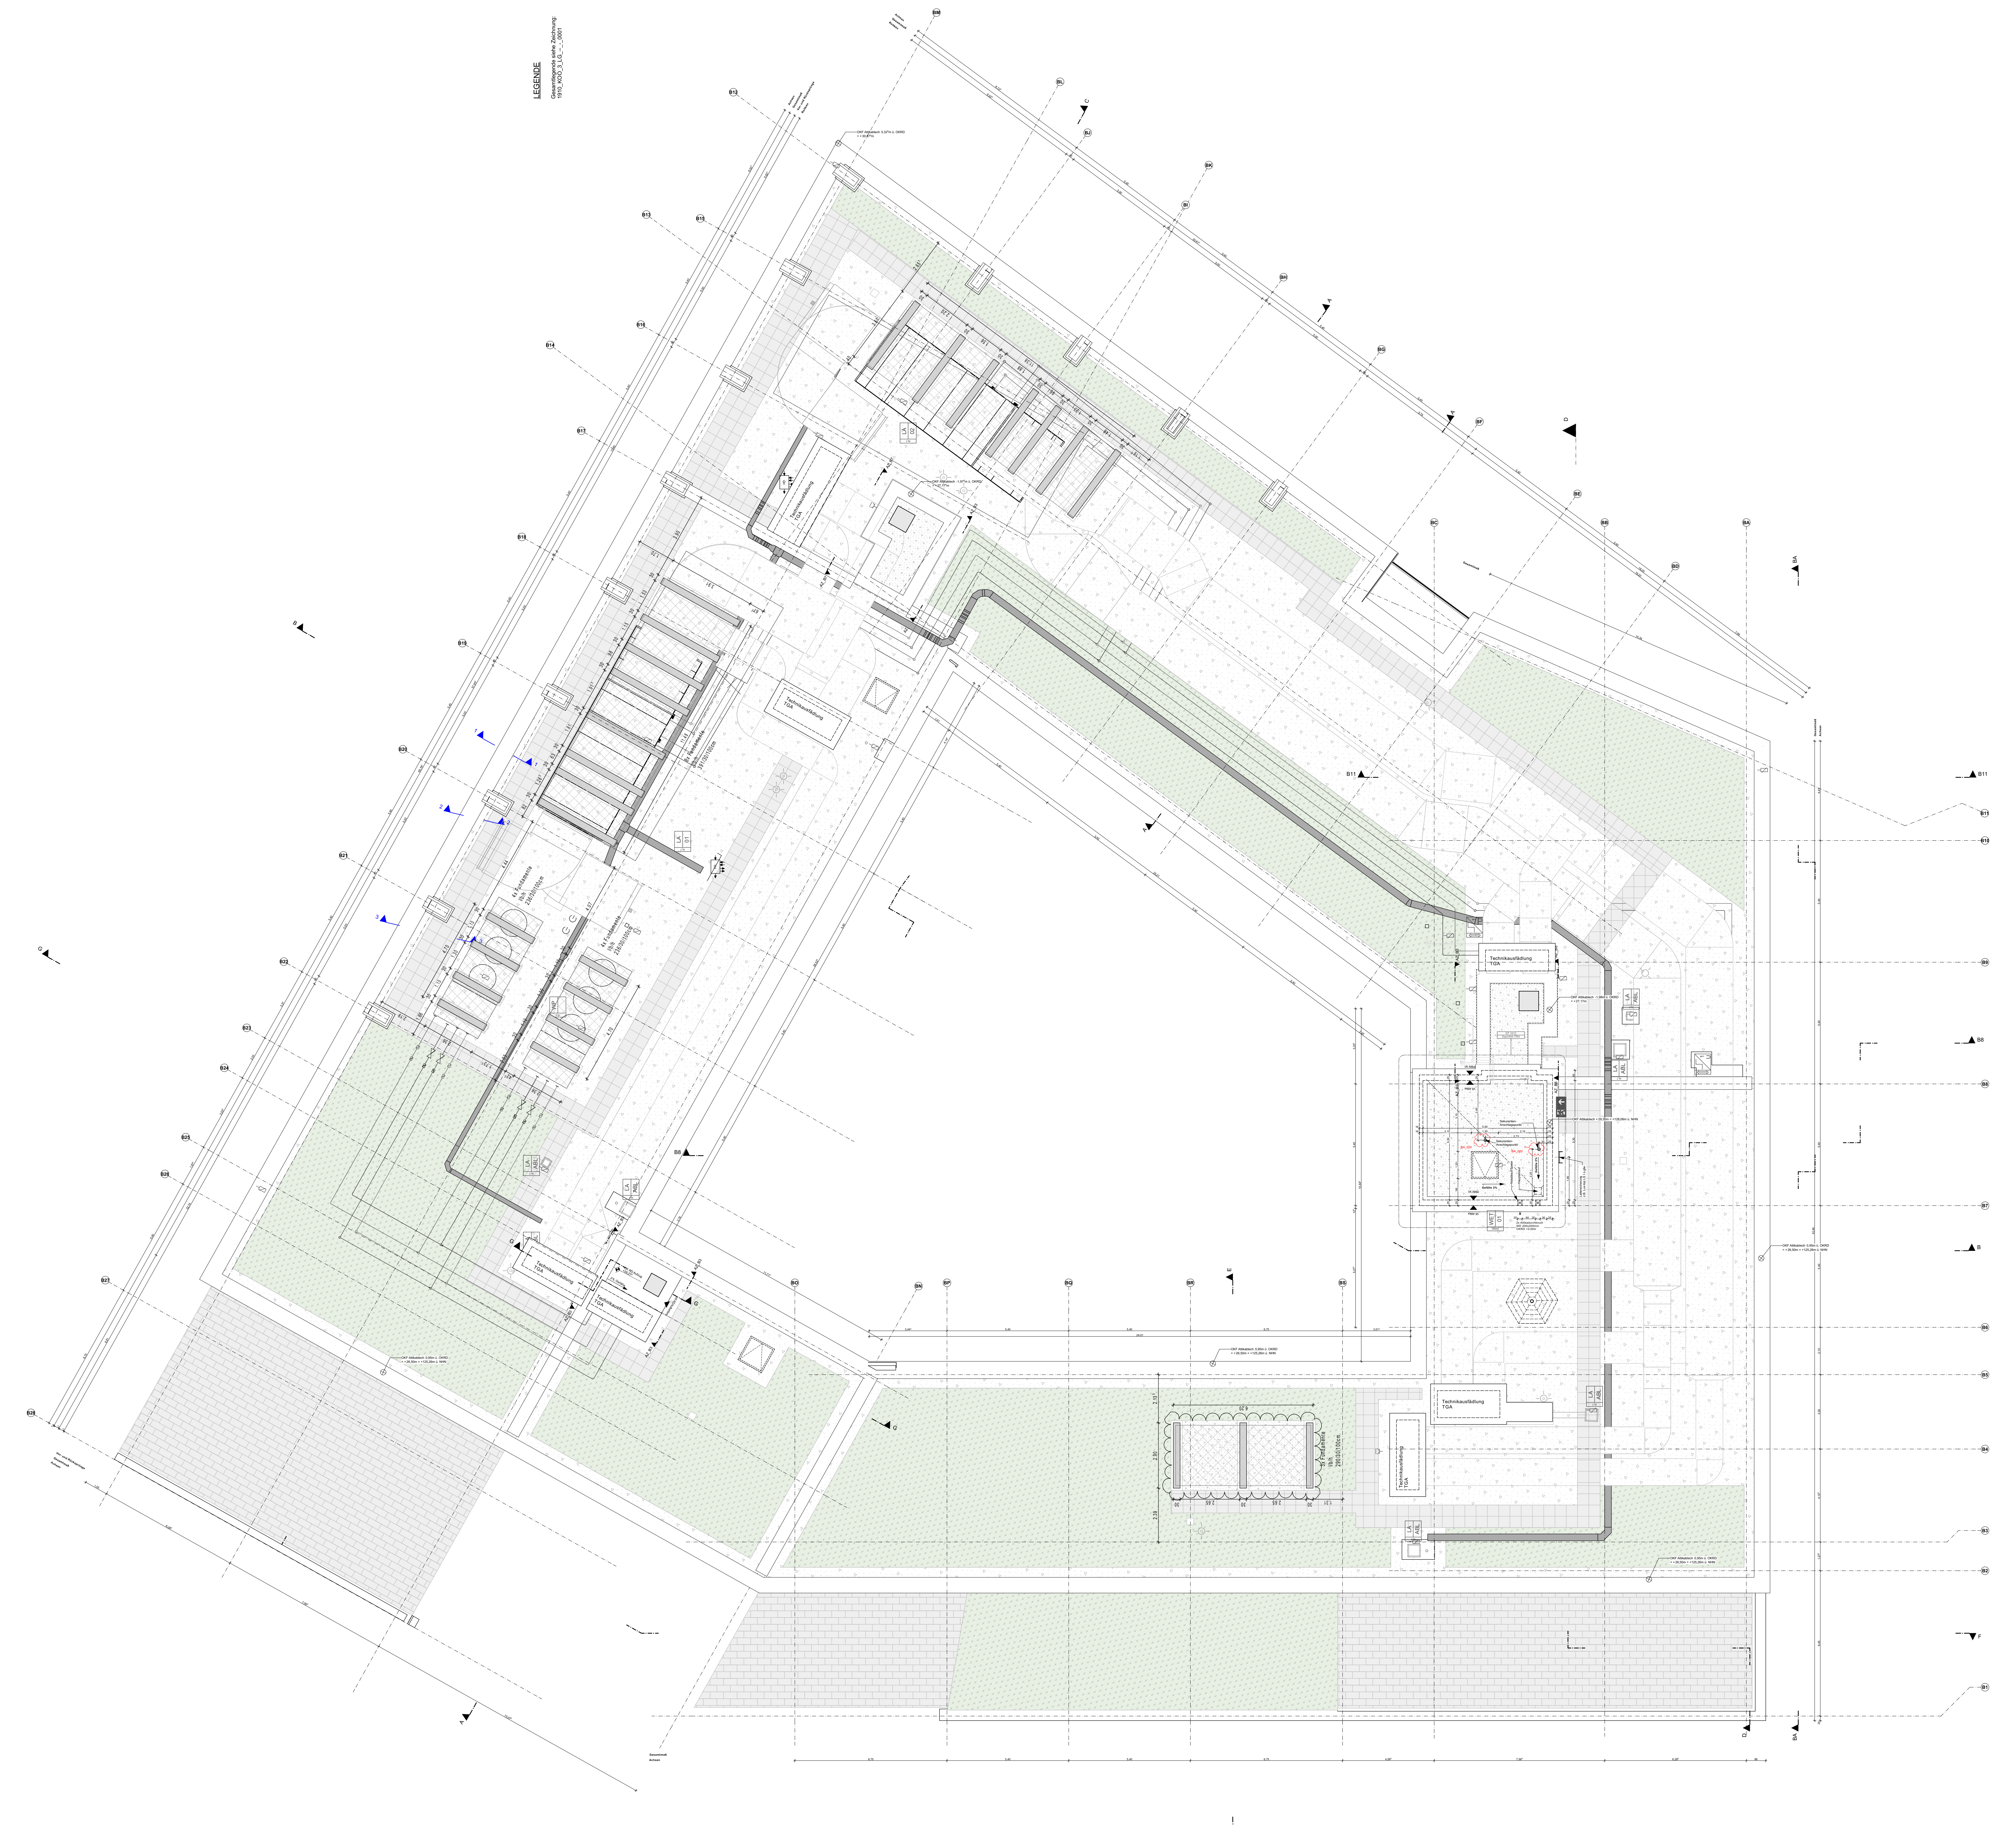
LEGENDE
Gesamtlegende siehe Zeichnung:
1910_KOO_3_LG_-_-_0001
B12
B13
B14
B15
B16
B17
B18
B19
B20
B21
B22
B23
B24
B25
B26
B27
B28
BM
BL
BJ
BK
BI
BH
BG
BF
BE
BC
BB
BD
BA
BO
BN
BP
BQ
BR
BS
B11
B10
B9
B8
B7
B6
B5
B4
B3
B2
B1
Achsen
Gesamtmaß
Vor- und Rücksprünge
Rohbau
OKF Attikablech 5,32m ü. OKRD = +30,87m
OKF Attikablech -1,97m ü. OKRD = +27,17m
OKF Attikablech 0,95m ü. OKRD = +26,50m = +125,26m ü. NHN
OKF Attikablech -1,98m ü. OKRD = +27,17m
OKF Attikablech +29,30m = +128,06m ü. NHN
Technikausfädlung TGA
8x Fundamente lb/h 391/30/100cm
4x Fundamente lb/h 236/30/100cm
3x Fundamente lb/h 290/30/100cm
LA 01
LA 02
LA ABL
WET 01
WP
Sekuranten-Anschlagpunkt
BA_020
Gefälle 2%
VK Attika
Notablauf Speier
Hauptablauf
Leitersicherung z.B. Lux-top LS II gdw
2x Attikadurchbruch WD 200x200mm OKRD +0,00m
DT 1012 Dach/WA-TRH
2% Gefälle
OK BD Aufzug
A
B
C
D
E
F
G
B8
B11
BA
1
2
3

Hinweise:
Leitdetails zur Vergabe der Bauleistungen sind für die Bauausführung nicht freigegeben.
Der Ausführende ist verpflichtet, den Auftraggeber auf etwaige Unstimmigkeiten der Ausführungsunterlagen hinzuweisen (VOB/B, 3.3). Alle Planunterlagen sind nur in Verbindung mit den zugehörigen Plänen des Architekten und der Fachingenieure gültig. Alle Maße sind vor Ausführung durch den AN zu prüfen und soweit erforderlich örtlich zu messen. Maßliche Differenzen sind vor der Ausführung mit der Objektüberwachung zu klären. Bedenken gegen die geplante Ausführung sowie Unstimmigkeiten in den Plänen und sonstigen Ausführungsunterlagen sind mit der Objektüberwachung vor Ausführung zu klären. Bei der Bauausführung sind die Planungen der Fachingenieure sowie die Angaben der Sonderfachleute zu beachten. Unstimmigkeiten zwischen den Plänen sind mit der Objektüberwachung zu klären. Angaben zu Installations- und Einbauteilen, die in die Stahlbetonkonstruktion einbetoniert werden, sowie Auflager und Anschlussdetails, sind den geprüften Plänen der beteiligten Fachplaner zu entnehmen. Aussparungen sind nach Montage unter Berücksichtigung der erforderlichen Schalldämm- und Brandschutzmaßnahmen zu schließen. Angaben zu Stahlbetonkonstruktionen und deren Anschlussdetails sind der Fachplanung (z.B. Schal und Bewehrungspläne) des Tragwerkplaners zu entnehmen. Schlitze und Durchbrüche, Kernbohrungen, Rohrhülsen, Wanddurchführungen etc. gemäß Angabe TGA und Tragwerksplanung.

Höhenbezüge:
- UK UZ bezogen auf OKFF - Brüstungshöhen OKFF bis OKR
- UK AHD bezogen auf OKFF - Türhöhen OKFF bis UKR

AHD	Abhangdecke	DV	Deckenversprung	LB	lichte Breite	UKR	Unterkante Roh
BD	Bodendurchbruch	E	Elektro	OK	Oberkante	UV	Unterverteilung
BE	Bodeneinlauf	EF	Estrichfuge	OKF	Oberkante Fertig	UZ	Unterzug
BK	Bodenkanal	ELT	Elektrotechnik	OKR	Oberkante Roh	ÜZ	Überzug
BRH	Brüstungshöhe	FB	Fussbodenbelag	RBV	Rohbodenversprung	VK	Vorderkante
BS	Bodenschlitz	FF	Fertigfussboden	RD	Rohdecke	WD	Wanddurchbruch
BW	Brandwand	FV	Festverglasung	RH	Rohrhülse	WH	Wandhydrant
BBW	Bauart Brandwand	F30/F90	Brandschutzanf. Wand	RL	Rollladen	WS	Wandschlitz
D	Drehflügel	HK	Heizkörper	RR	Regenfallrohr	WU	wasserundurchlässig
DB	Deckenbelag	HKV	Heizkreisverteiler	RS	Rauchschutztür	Ⓕ	Feuerlöscher
DD	Deckendurchbruch	K	Kippflügel	SO	Sonnenschutz		
DF	Dehnungsfuge	KB	Kernbohrung	TP	Trockenputz		
DK	Dreh-,Kippflügel	KL	Klappflügel	T30/T90	Brandschutzanf. Tür		
DS	Deckenschlitz	i.Li	im Lichten	UK	Unterkante		
DT	dichtschliessend	LH	lichte Höhe	UKF	Unterkante Fertig		

▨	Stahlbeton Stb	▦	Stb Fertigteil	▩	Dämmung hart	—	Geschnittenes Bauteil Stahlbeton
▨	WU Beton	☐	Bestand	▩	Dämmung weich	—	Geschnittenes Bauteil Mauerwerk
▨	Unbewehrter Beton	☐	Trockenbau	▨	Naturstein	—	Geschnittenes Bauteil Sonst
▨	Mauerwerk MW	▨	Erdreich			—	Ansichtslinie
						- - -	verdeckte Kanten unter Schnitt
						- - -	verdeckte Kanten über Schnitt

OKFF
OKRD
OKFF
OKRD
B Schnittbezeichnung
Ⓐ Achsbezeichnung
Ⓐ Ausbauachsen (blau)
Änderungswolke
Klärungswolke ohne Freigabe
1300 Fassade — Detail-/Zeichnungsnr. Zeichnungsinhalt
DT 7101-7104 Think Thanks — Detail-/Zeichnungsnr. Zeichnungsinhalt

Ausbaustempel:
Wandoberflächenqualitäten
Abhangdeckentyp
Bodenaufbau
2 AD-01b BA-21a 12 2 2

Wandoberflächenqualitäten:
02 - Q2 gespachtelt
12 - Glas/ Systemtrennwand

WI_35.F 90 A.≥53dB; g
Wandetikett bestehend aus:
Wandtyp.Brandschutzqualität.Schallschutzanforderung.
g = gleitender Deckenanschluss

Vorabzug WP2

INDEX	DATUM	Gezeichnet von	ÄNDERUNGEN
02	20.06.2022	ahi	TGA Gerätefundamente ü. Dach ergänzt, Sekuranten-Anschlagspunkt ergänzt
01	18.03.2022	ahi	Aufmauerung um TGA Durchbruch ü. Dach ergänzt, Steigleiter für TRH-Dach ergänzt
00	21.02.2022	ahi	Fortführung Planung

PLANKENNUNG BASISPLAN (INDEX)
DATUM BASISPLAN (INDEX)

PLANBEZEICHNUNG
WP2
Bauteil B - Übersichtsplan Dachaufsicht

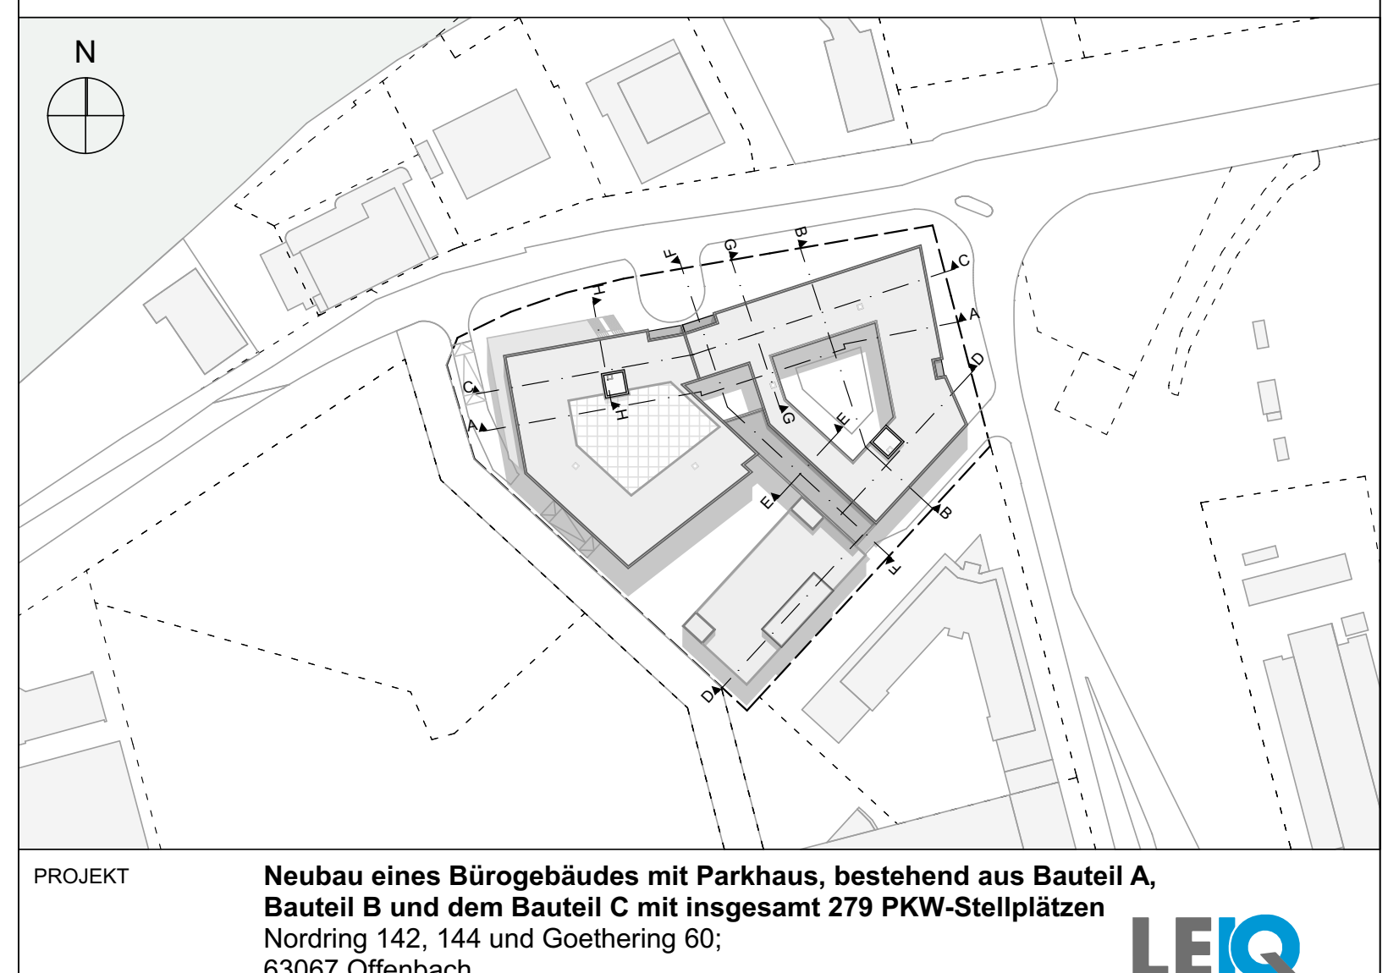

PROJEKT
Neubau eines Bürogebäudes mit Parkhaus, bestehend aus Bauteil A, Bauteil B und dem Bauteil C mit insgesamt 279 PKW-Stellplätzen
Nordring 142, 144 und Goethering 60;
63067 Offenbach

LEIQ

BAUHERR
HTO Nordring 1 GmbH
Theodor-Heuss-Str. 53-63; 61118 Bad Vilbel
Tel.: +49 40 280 9520

GU
Adolf Lupp GmbH + Co KG
Alois-Thums-Straße 1-3; 63667 Nidda
www.lupp.de

ARCHITEKT
holger meyer gmbh
Eschersheimer Landstraße 50-54, 60322 Frankfurt
Tel.: +49 69 264 948 700
www.hma.archi

holger meyer
architektur

TWP FP-PLANER: **Ingenieurbüro Federlein,** Saaleblick 2, 97616 Salz
HLSK FP-PLANER: **BAE-GmbH,** Am Hofbräuhaus 1, 96450 Coburg
ELEKTRO FP-PLANER: **Elektroplanung Schweizer,** Eibenstraße 3, 74582 Gerabronn
FASSADENPLANUNG: **Priedemann Fassadenberatungs GmbH,** Am Wall 17, 14979 Berlin

PROJEKT NR.	LEISTUNGSPHASE	GEZEICHNET / DATUM	GEPRÜFT / DATUM
1910	5	ahi 04.01.2022	
MASSSTAB	BLATTGRÖSSE	HÖHENKOTEN ± 0,00NHN	
1:100	DIN A0 (841 x 1189)	± 0,00 = 98,76 m ü. NHN	

PLANBEZEICHNUNG
Bauteil B - Übersichtsplan Dachaufsicht
WP2

BIMcloud: VSRV19 - BIMcloud Basic für ARCHICAD 24/1910 NOR/1910 Layouts LP5

PLANNUMMER	1 Planer	2 Fachbereich	3 LPH	4-5 Planinhalt	6 Ort	7-8 Baut.+Bs.	9 Blatt-Nr.	10 Index	11 Status

HMA-ARC-5-UP-WP-08-B0-0001-02-v